


4

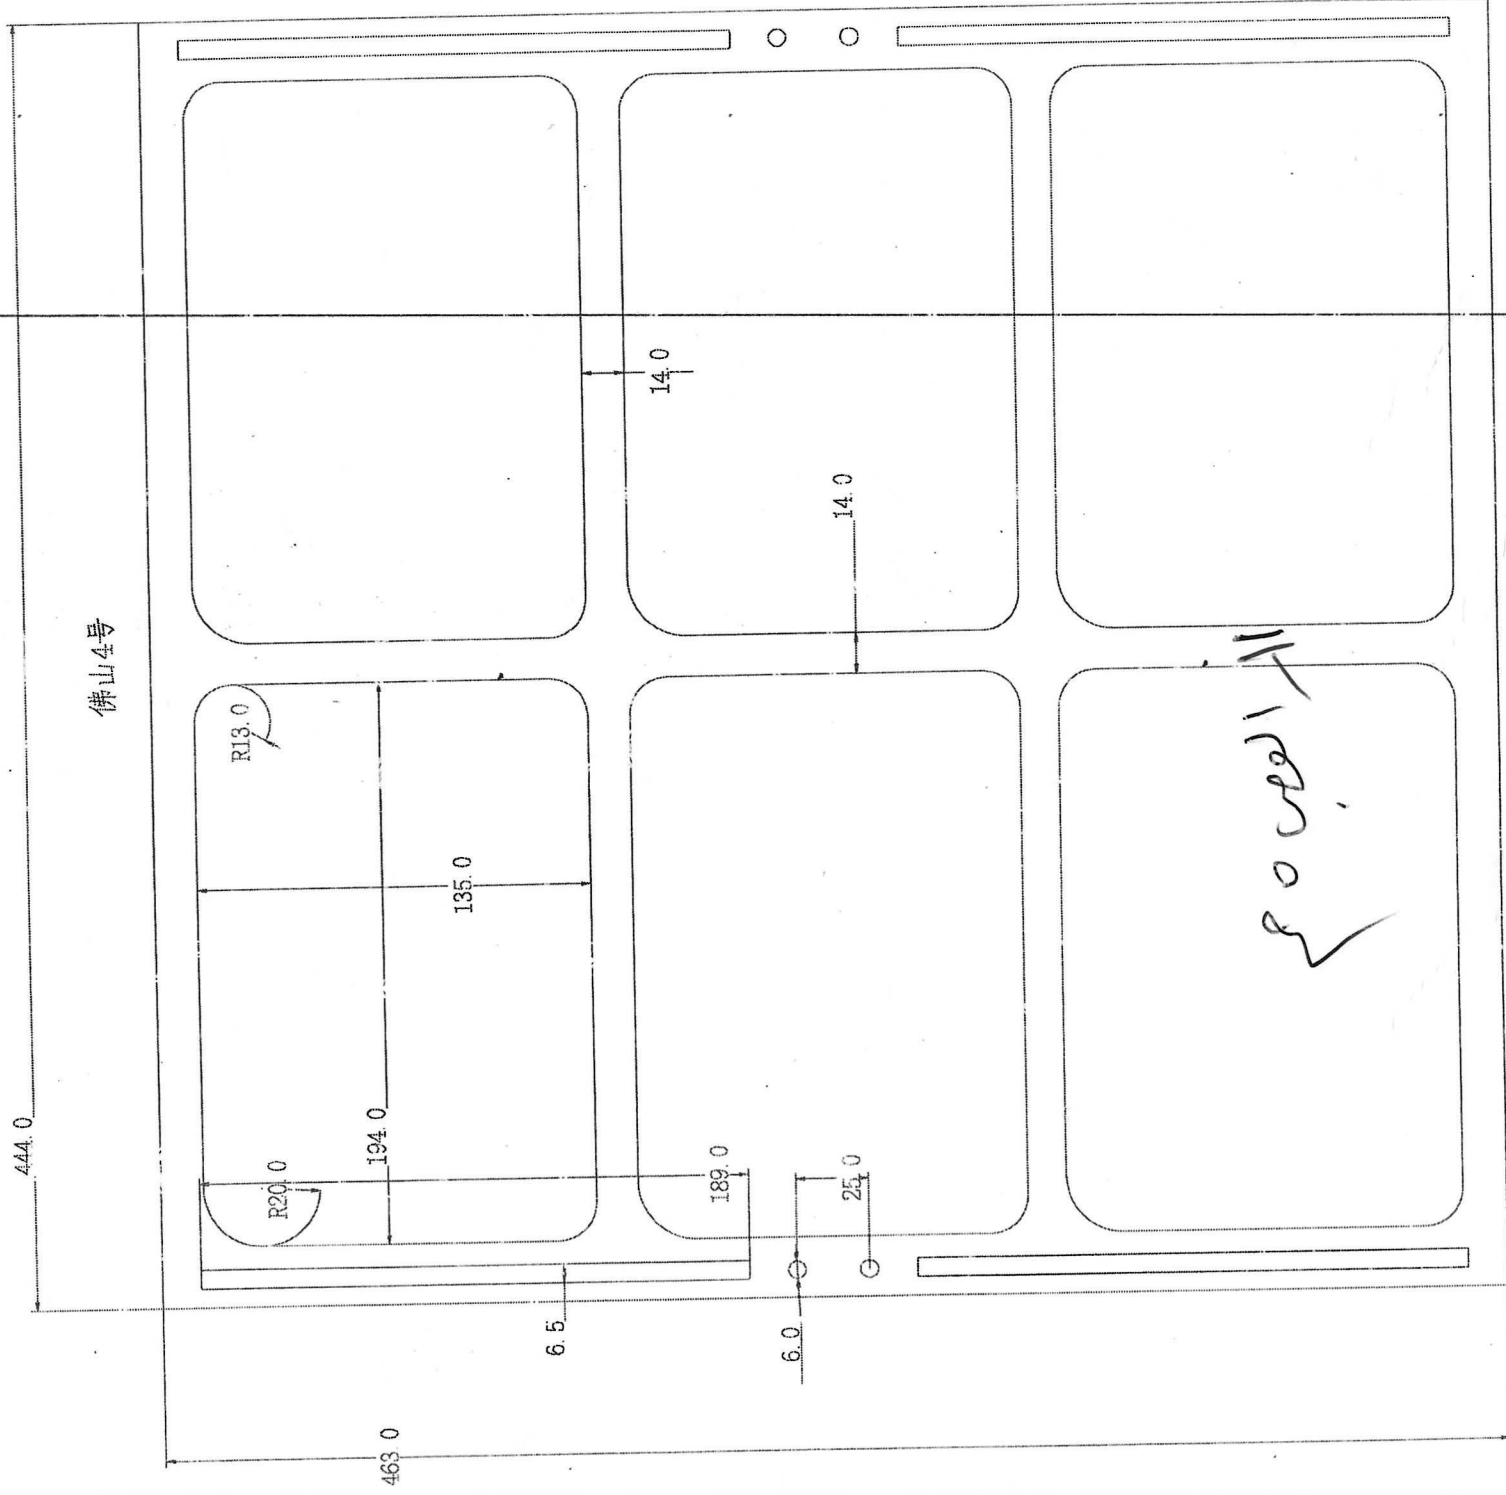

佛山4号